

הערה- החוברת מוגשת לצורך מכרז קבלנים
פרטי גמר, חיפויים ופריסות יושלמו ויועדכנו בהמשך לאחר השלמת הרכישה ע"י הלקוחות



HADAR GLIKSMAN SHOCHAT
INTERIOR DESIGN STUDIO
054-7508054
hadar.glikzman@gmail.com

משפחת קריזר אהרון סט תכניות אדריכליות

תאריך: 06.08.2026

כתובת הפרוייקט: הסבוראים 5, תל אביב

טלפון הלקוח: 050-4816685

טלפון המתכננת: 054-7508054


"The details are not the details. They make the design". Charles Eames



<
--




HADAR GLIKSMAN SHOKHAT
INTERIOR DESIGN STUDIO
054-7508054
hadar.gliksman@gmail.com

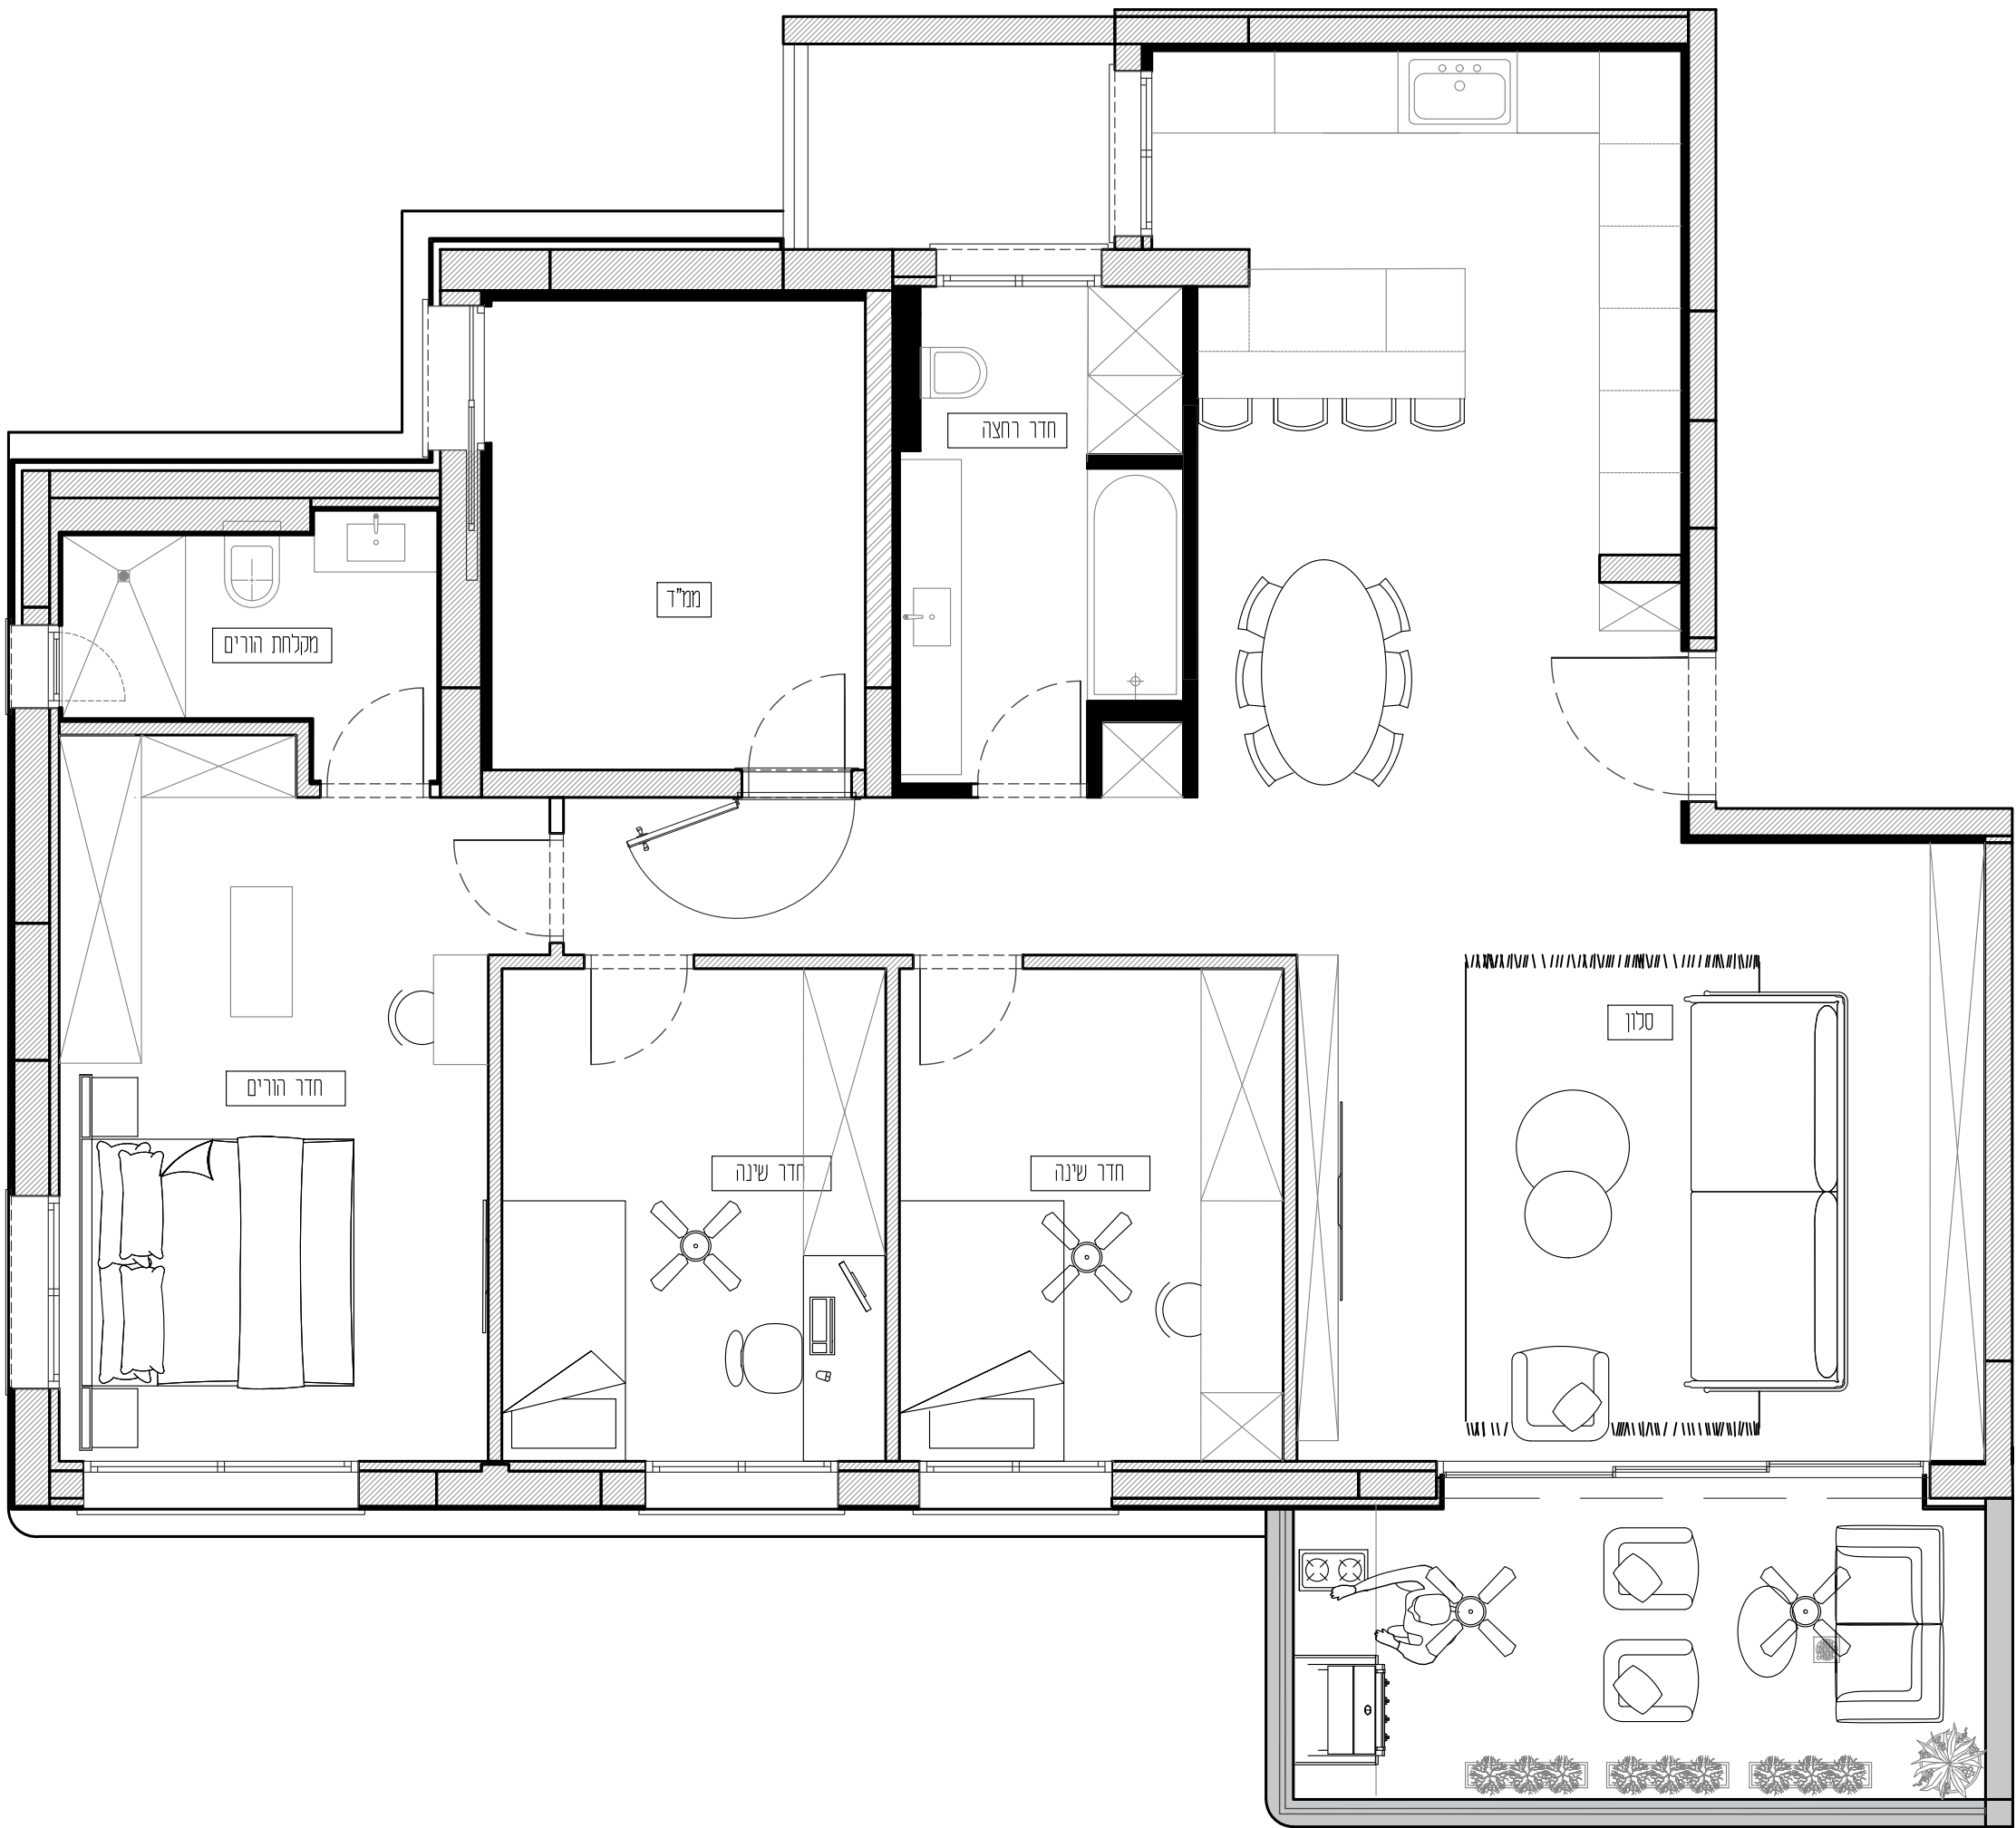

הערות			מעקב שינויים			תכנית: העמדת ריהוט		לקוח: ענבל ותומר	
			מס'	תאריך	תיאור השינוי	גיליון מס':		כתובת: הסבוראים 5 תל אביב	
			1.		1. על המבצע לבדוק את התאמת התכנית בשטח, לפני הבניה, ולבקר את המידות. על כל סעות ואז אי התאמה יש לעדכן משרד מתכנן.	גודל גיליון: A2		06.08.2026	
			2.		2. אין לקבוע מידות עפ"י שרטוט. המידות המצויבות הן מידות שנמדדו בשטח לאחר ביצוע	1:50			
			3.		3. המידות בתכנית הן ברוטו - ללא חיפוי גמר				
			4.		4. יתכנו שינויים בהתאם להוראות הביצוע הסופי				
			5.		5. כל התכניות נשארות רכוש המתכנן: אין לעשות בהן שימוש ללא אישור בכתב מהמתכנן				
			6.		6. כל התערוכות חקמות אלא אם צוין אחרת				
			7.						
						חתימת הלקוח לאישור התכנית:			
						לעיון		לאישור	
						למכרז		לביצוע	



HADAR GLIKSON STUDIO
INTERIOR DESIGN STUDIO
054-750854
hadar.glikson@gmail.com

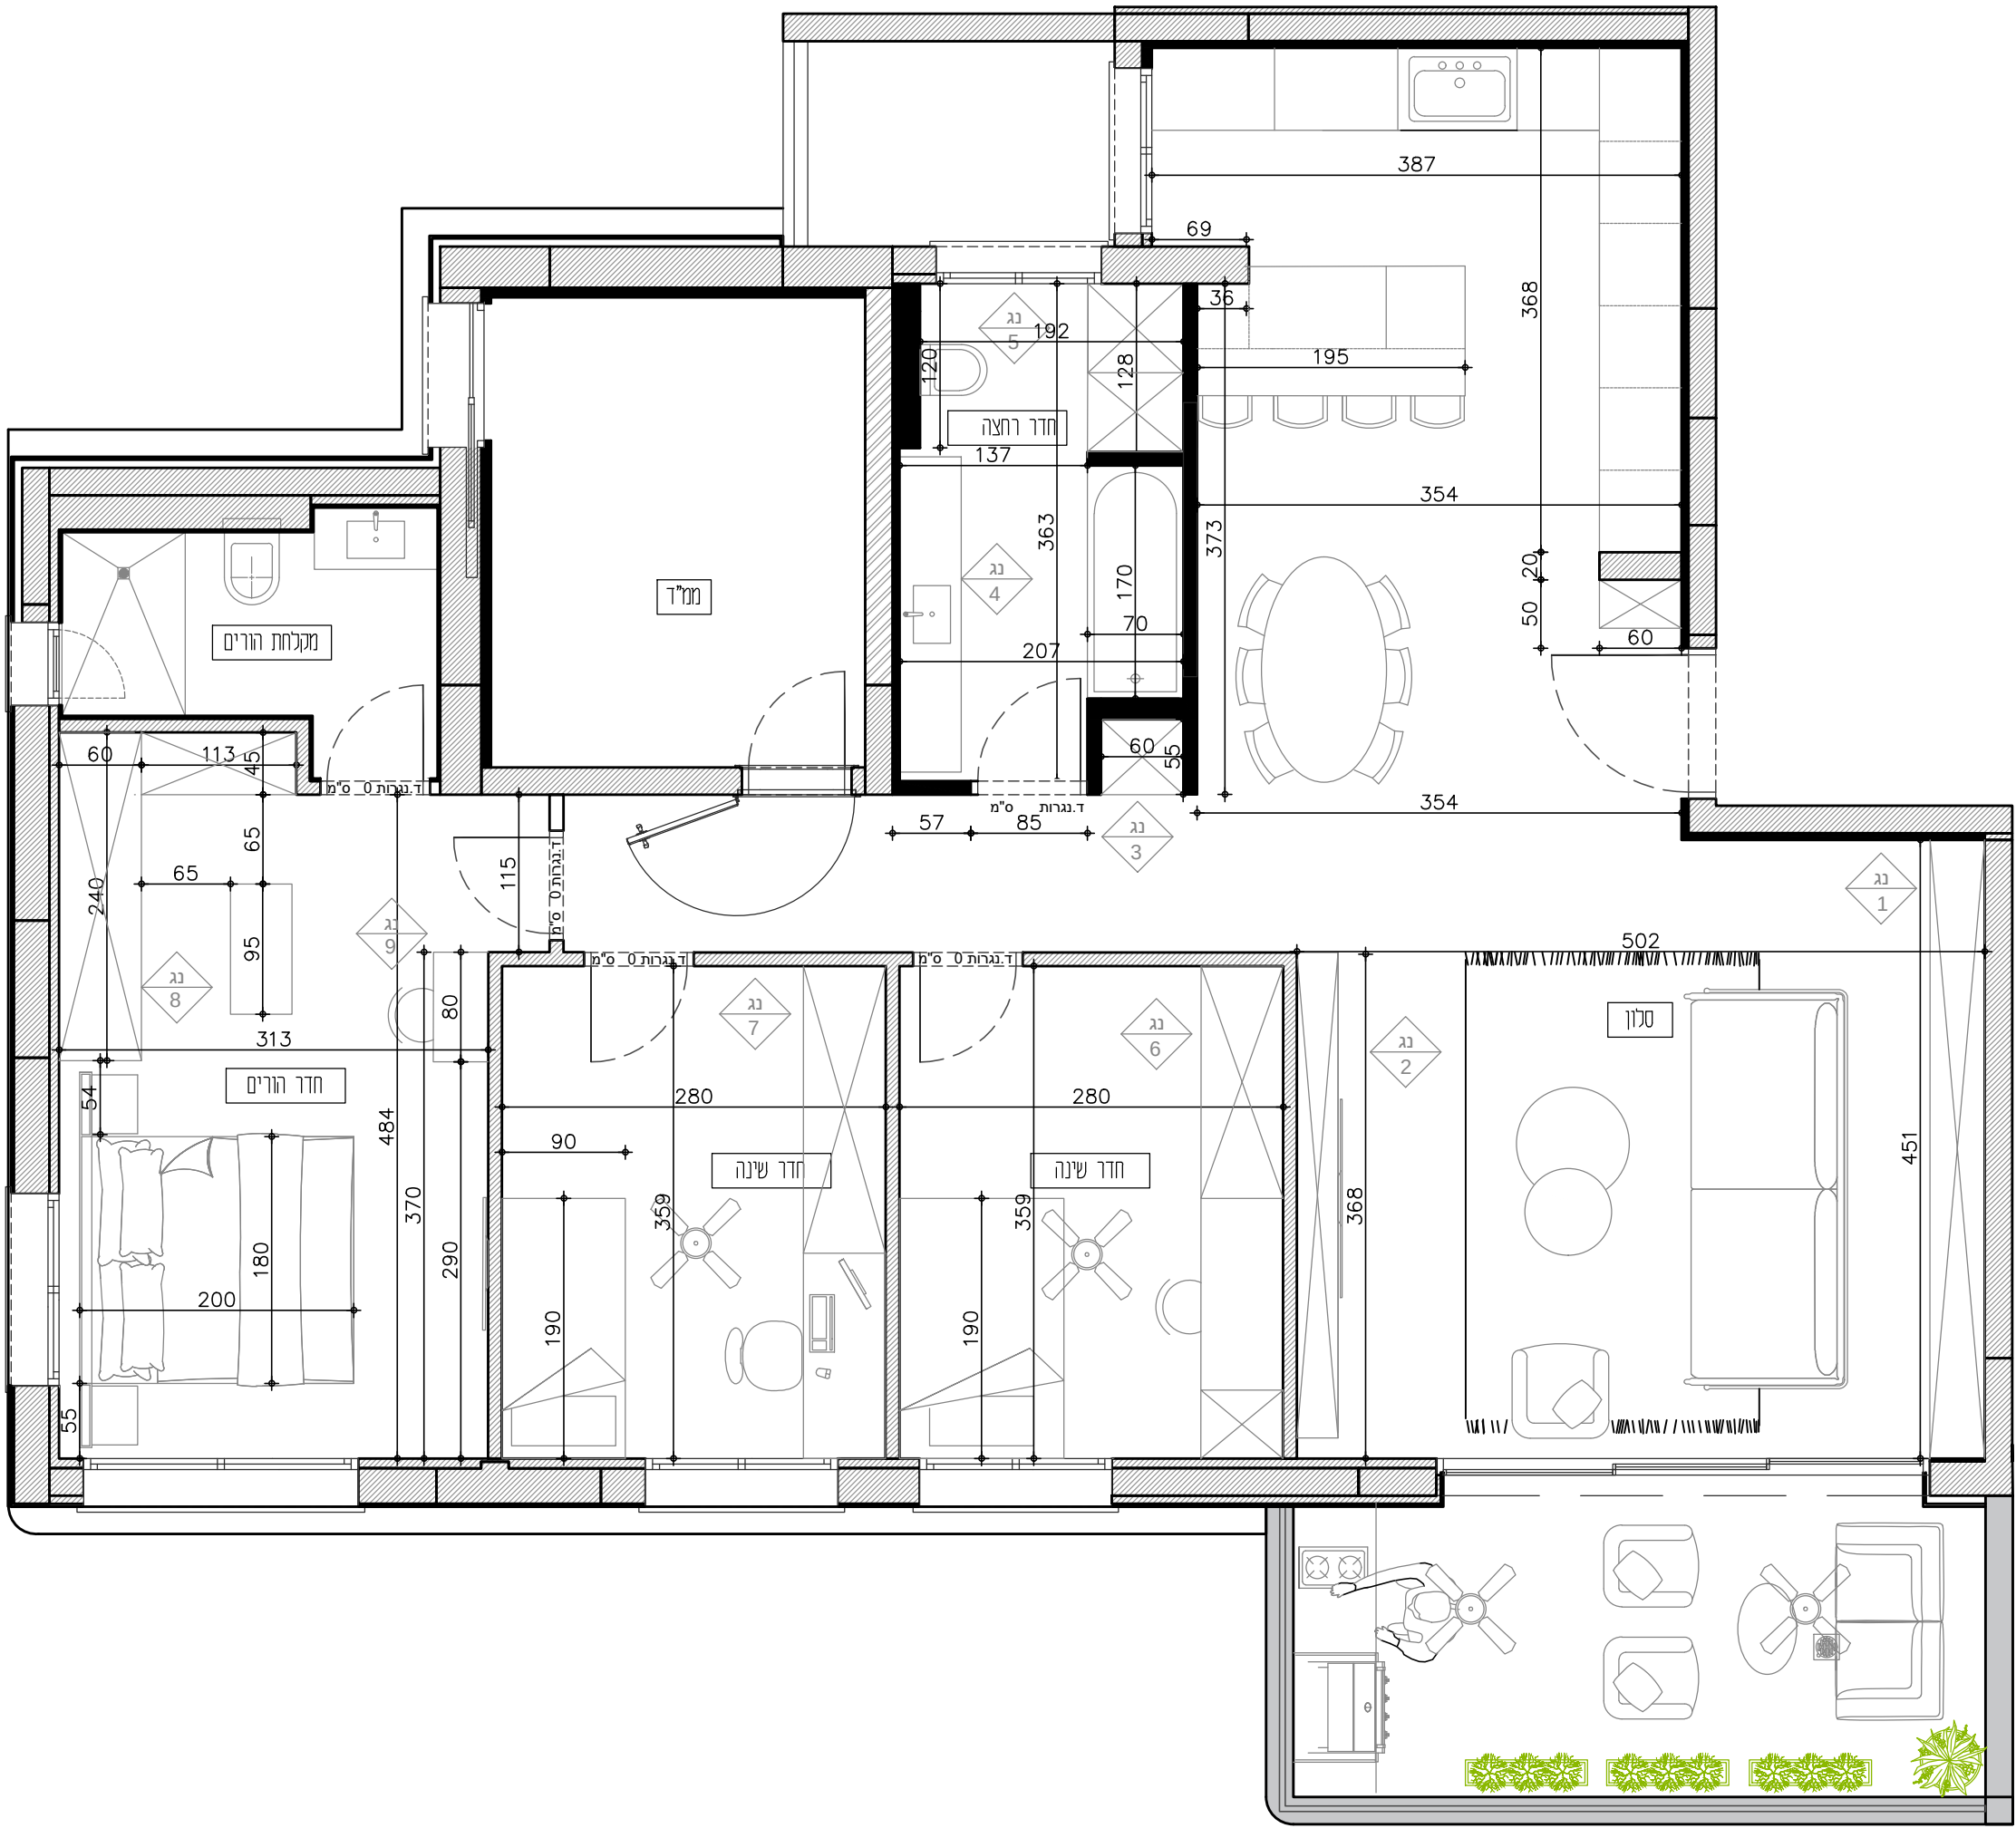

הערות

מעקב שינויים

HG HADAR GLIKSMAN SHOCHAT INTERIOR DESIGN STUDIO 054-7508054 hadar.gliksman@gmail.com	לקוח: ענבל ותומר		תכנית: ת.אדריכלית	
	כתובת: הסבוראים 5 תל אביב		גיליון מס':	
	05.08.2026		קנ"מ: 1:50	
	גודל גיליון: A2			
	חתימת הלקוח לאישור התכנית:			
	☒ לעיון ☐ לאישור ☐ למכרז ☐ לביצוע			

מעקב שינויים		הערות
מס'	תאריך	תיאור השינוי
1.		
2.		
3.		
4.		
5.		
6.		
7.		

1. על המבצע לבדוק את התאמת התכנית בשטח, לפני הבניה, ולבקר את המידות. על כל טעות ואו אי התאמה יש לעדכן משרד מתכנן.

2. אין לקבוע מידות עפ"י שרטוט. המידות המחייבות הן מידות שנמדדו בשטח לאחר ביצוע


3. המידות בתכנית הן ברוטו - ללא חיפוי גמר

4. יתכנו שינויים בהתאם להוראות הביצוע הסופי

5. כל התכיות נשארות רכוש המתכנן: אין לעשות בהן שימוש ללא אישור בכתב מהמתכנן

6. כל ההערות תקפות אלא אם צוין אחרת

- על המבצע לבדוק את התאמת התכנית בשטח, לפני הבניה, ולבקר את המידות. על כל טעות ואז אי התאמה יש לעדכן משרד מחכנו.
- אין לקבוע מידות עפ"י שרטוט. המידות המחיבות הן מידות שנמדדו בשטח לאחר ביצוע.
- המידות בתכנית הן ברוטו - ללא חיפוי גמר.
- יחבנו שינויים בהתאם להוראות הביצוע הסופי.
- כל התכניות נשארות רכוש המחכנו: אין לעשות בהן שימוש ללא אישור בכחב מחכנו.
- כל התערבות חקמות אלא אם צוין אחרת.

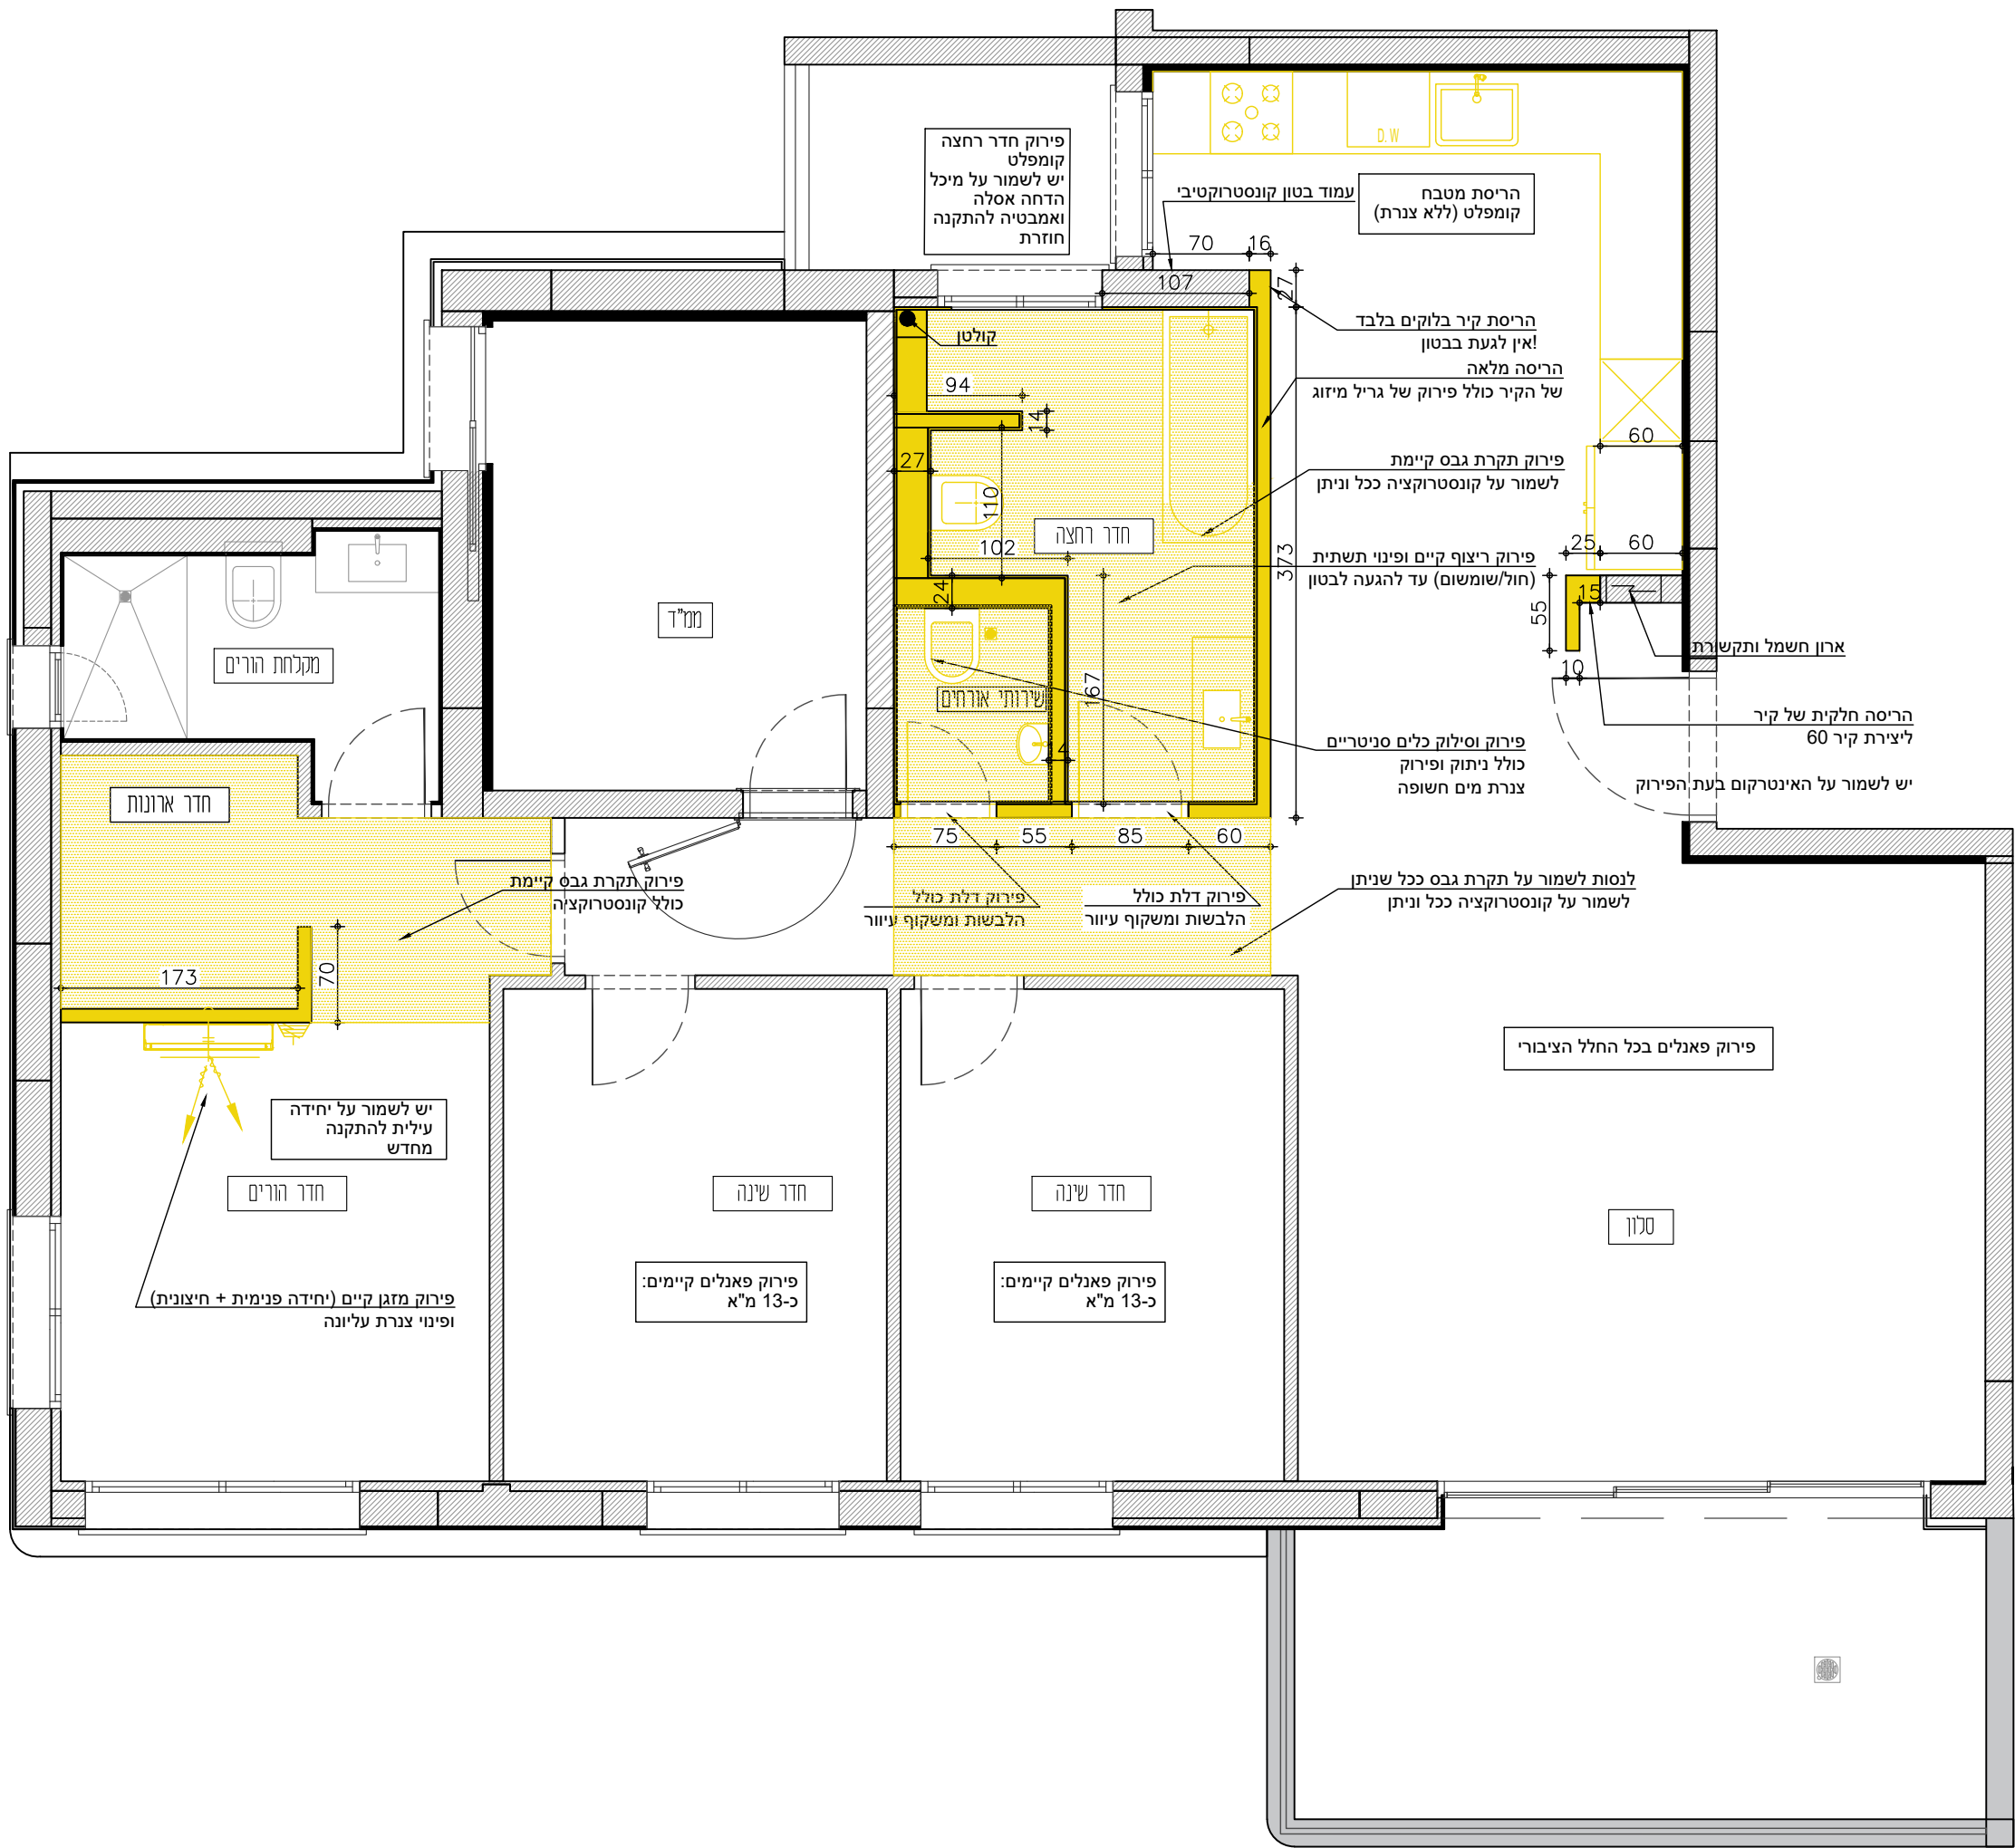

קיים להריסה		מס'תאריך 1. 2. 3. 4. 5. 6. 7.		מקרא הריסה הערות	
לקוח: ענבל ותומר תכנית: הריסה		כתובת: הסבוראים 5 תל אביב גיליון מס':		חתימת הקווקח לאישור התכנית:	
06.08.2026 קנ"מ: 1:50 גודל גיליון: A2		לעיון לאישור למכרז לביצוע			

קיים

להריסה

מס'תאריך

1.

2.

3.

4.

5.

6.

7.

מקרא הריסה

הערות

לקוח: ענבל ותומר

תכנית: הריסה

כתובת: הסבוראים 5 תל אביב

גיליון מס':

06.08.2026

קנ"מ: 1:50

גודל גיליון: A2

חתימת הקווקח לאישור התכנית:

לעיון

לאישור

למכרז

לביצוע

קיים

להריסה

מס'תאריך

1.

2.

3.

4.

5.

6.

7.

מקרא הריסה

הערות

לקוח: ענבל ותומר

תכנית: הריסה

כתובת: הסבוראים 5 תל אביב

גיליון מס':

06.08.2026

קנ"מ: 1:50

גודל גיליון: A2


חתימת הקווקח לאישור התכנית:

לעיון

לאישור

למכרז

לביצוע

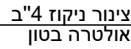



	שקע חשמל
	שקע מוגן מים
	שקע כח
	שקע כח מוגן מים
	שקע חד פאזי \ חלח פאזי
	שקע USB
	נקודת רשת (אינטרנט)
	נקודת כלפון \ נקודת טלוויזיה
	מזגן
	נקודה למכור חומריגור
	לוח חשמל
	לוח תקשורת
	לחצן מעמון 110 h=110
	מעמון דירתי 230 h=230
	חונה לוונסה
	חיווט בבגס
	צינור קוברה לחשמלה
	חונה לטיב אופטי מרגילר

	קופסת שקעים עם צינור גישור: 3 שקעים + 1 רשת 8 שקעים + 2 רשת
	עומדת מחשב: 2 שקעים + USB 1 4 שקעים + USB 2 2 לחקשורת
	צינור קוברה

גלאים	עשן	גז	חום	נפח	וילון	מסמ דלתאלין
אכטרה	פאנל בקרה	פעלמה	פדלמות ריכוז	צופר	אינטרקום	אינטרקום
	רסקול \ רסקול מגן מים	סאב	R	ריכוז רסקולים		



לקוח: ענבל ותומר	תכנית: חשמל
כתובת: הסבוראים 5 תל אביב	גיליון מס':
05.08.2026	קנ"מ: 1:50
גודל גיליון: A2	
חתימת הלקוח לאישור התכנית:	
☒ לעיון	☐ לאישור
☐ למכרז	☐ כביצוע

- עד המבצע לבדוק את החמאם התכנית בשטח, לפני הבניה, ולבקר את המידות. על כל געות וואו אי החמאם יש לעדכן משרד מתכנן.
- אין לקבוע מידות עפ"י שרטוט. המידות המחייבות הן מידות שממדדו בשטח לאחד ביצוע
- המידות בתכנית הן ברטו - ללא חיפוי גמר
- יחבנו שינויים ברחאם להוראות הביצוע הסופי
- כל החכניות נשארות רכוש המחכנן: אין לעשות בהן שימוש ללא אישור בכתב מהמחכנן
- כל ההערות תקפות אלא אם צויין אחרת

מס'	תאריך	תיאור השינוי
1.		
2.		
3.		
4.		
5.		
6.		
7.		

- חוקי ברזל ומידות
 - אפש מריצוי: כל מידות הגובה מחייטות למסלט ריצוי מוגמר
 - מיקום מרחבי: כל המידות (אורך וגובה) מחייטות למרכז קופסת החשמל
 - מרחקים: יש לשמור על מרחק מינימלי של 15 ס"מ מפינות קיר או משקופים
- גבהים סטנדרטיים
 - שקעים: גובה שקעים כלליים: 50 ס"מ \ מעל מטבח עבודה: 10 ס"מ
 - מחגים: גובה מחגי תאורה ועליטה: 10 ס"מ
 - מגן: גובה שקע למגן עילי: 40 ס"מ מרחקרה \ הנמכת הגבס
- החיות התקנה ואביזרים
 - איחוד קופסאות: חובה לאגד מחגים ושקעים סמוכים לקופסת חיבורים
 - משוחמת (קופסאות 16x4x3 מקום וכזו) ולדקפיד על פילוס מוחלט
 - הגנה ממים: כל אביזרי החשמל והתאורה בתחדים רטובים ובתצר יהיו מוגני מים. שקעים מוגני מים יותקנו בגובה מינימלי של 120 ס"מ
 - סוג אביזרים: כל אביזרי הקצצה יהיו תוצרת "גוויס", "סוויץ" (ניסקו) או שווה ערך, בתיאום ואישור הלקוח והמעצבת - סרם הרכישה

הערות

- כל ההערות והגבהים מרחקים תקפים אלא אם צויין אחרת
- יש להימנע עם מעצבת מים לצורך סימוני נקודות חשמל
- מיקום המזגנים המצויין בתכנית אינו סופי ויקבע עפ"י החלטתו של יועץ מיזוג



	מפסק, תאורה בודד
	מפסק תאורה מחליף \ מפליב
	מפסק תאורה מוגן מים - בודד \ כפול
	מפסק, יחיד מואר נלדוד, מחסם וכזו
	מפסק, לחריסאולון חשמלי
	דימר - מפסק לעמעום
	גוף תאורה תקרתי
	גוף תאורה תקרתי מוגן מים
	גוף תאורה צמוד קיר
	גוף תאורה צמוד קיר מוגן מים
	גוף תאורה שקוע בתקרה \ שקוע ברצפה \ שקוע בקיר
	מאוורר תקרה + תאורה
	תאורת חוץ מוגנת מים
	תאורת חירום קירית \ תקרתית
	סמט
	הזנה לפס לד



לקוח: ענבל ותומר		תכנית: תאורה	
כתובת: הסבוראים 5 תל אביב		גיליון מס':	
05.08.2026		קנ"מ: 1:50	גודל גיליון: A2
חתימת הלקוח לאישור התכנית:			
לעיון לאישור למכרז כביצוע			

- על המבצע לבדוק את התאמת התכנית בשטח, לפני הבניה, ולבדוק את המידות. על כל טעות וואו אי התאמה יש לעדכן משרד מתכנן.
- אין לקבוע מידות עפ"י שרטוט. המידות המחייבות הן מידות שנמדדו בשטח לאחר ביצוע
- המידות בתכנית הן ברטו - ללא חיפוי גמר
- יחבנו שינויים בהתאם להוראות הביצוע הטיפי
- כל התכניות נשארות רכוש המתכנן: אין לעשות בהן שימוש ללא אישור בכתב מהמתכנן
- כל ההערות תקפות אלא אם צויין אחרת


מעקב שינויים


מס'	תאריך	תיאור השינוי
1.		
2.		
3.		
4.		
5.		
6.		
7.		

- חוקי ברזל ומידות
 - אפש מריצוף: כל מידות הגובה מתייחסות למפלס ריצוף מוגמר
 - מיקום מרחבי: כל המידות (אורך וגובה) מתייחסות למרכז קופסת החשמל
 - מרחקים: יש לשמור על מרחק מינימלי של 15 ס"מ מפינוי קיר או משקופים
- גבהים סטנדרטיים
 - שקעים: גובה שקעים כלליים: 50 ס"מ \ מעל מטבח עבודה: 100 ס"מ
 - מתגים: גובה מתגי תאורה ועליהם: 100 ס"מ
 - מגן: גובה שקע למגן עילי: 40 ס"מ מרחקתרה \ הנמכת הגבס
- החיות התקנה ואביזרים
 - איחוד קופסאות: חובה לאגד מתגים ושקעים סמוכים לקופסת חיבורים
 - מחשבת (קופסאות 140 ס"מ) מקום וכזו ולדקפיד על פילוס מוחלט
 - הגנה מים: כל אביזרי החשמל והתאורה בתדרים רטובים ובתציר יהיו מוגני מים. שקעים מוגני מים יותקנו בגובה מינימלי של 120 ס"מ
 - סוג אביזרים: כל אביזרי הקצה יהיו תוצרת "גוויס", "סוויץ" (ניסקו) או שווה ערך, בתיאום ואישור הלקוח והמעצבת - סרם רכישתה

הערות

- כל ההערות והגבהים מתקנים תקפים אלא אם צויין אחרת
- יש להימנע עם מעצבת מים לצורך סימוני נקודות חשמל
- מיקום המזגנים המצוין בתכנית אינו סופי ויקבע עפ"י החלטתו של יועץ מיזוג

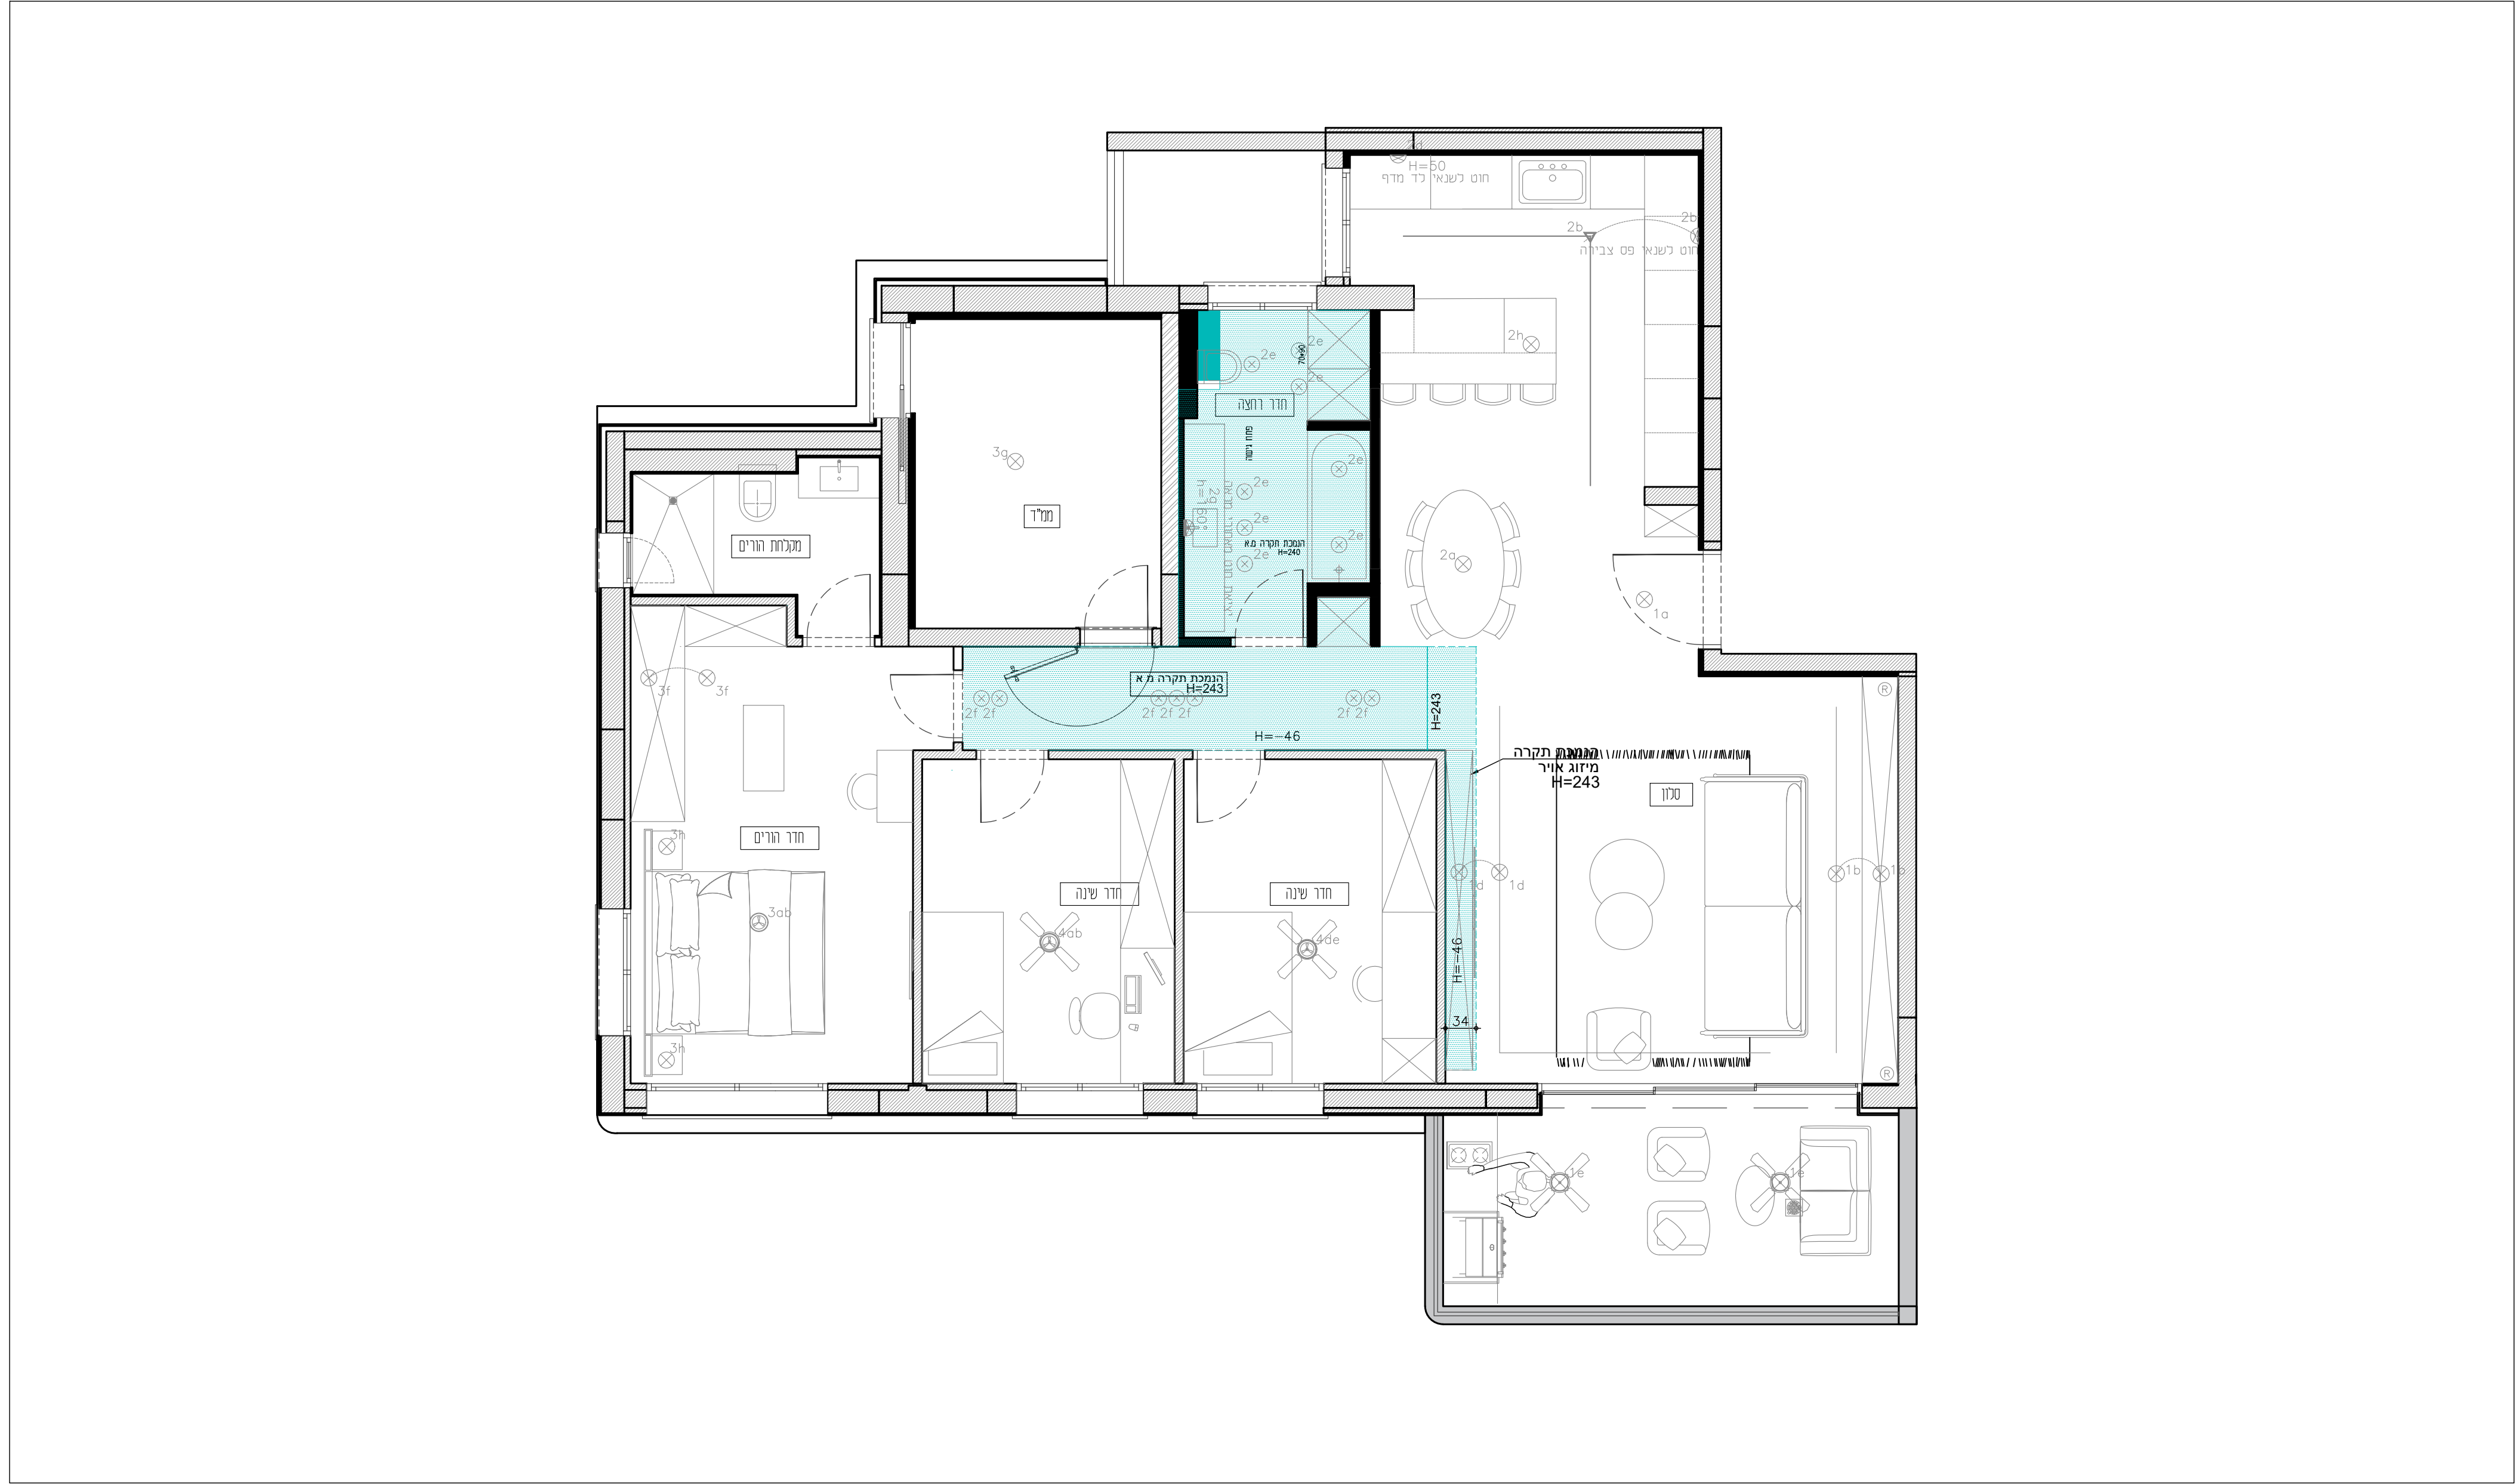[illegible]

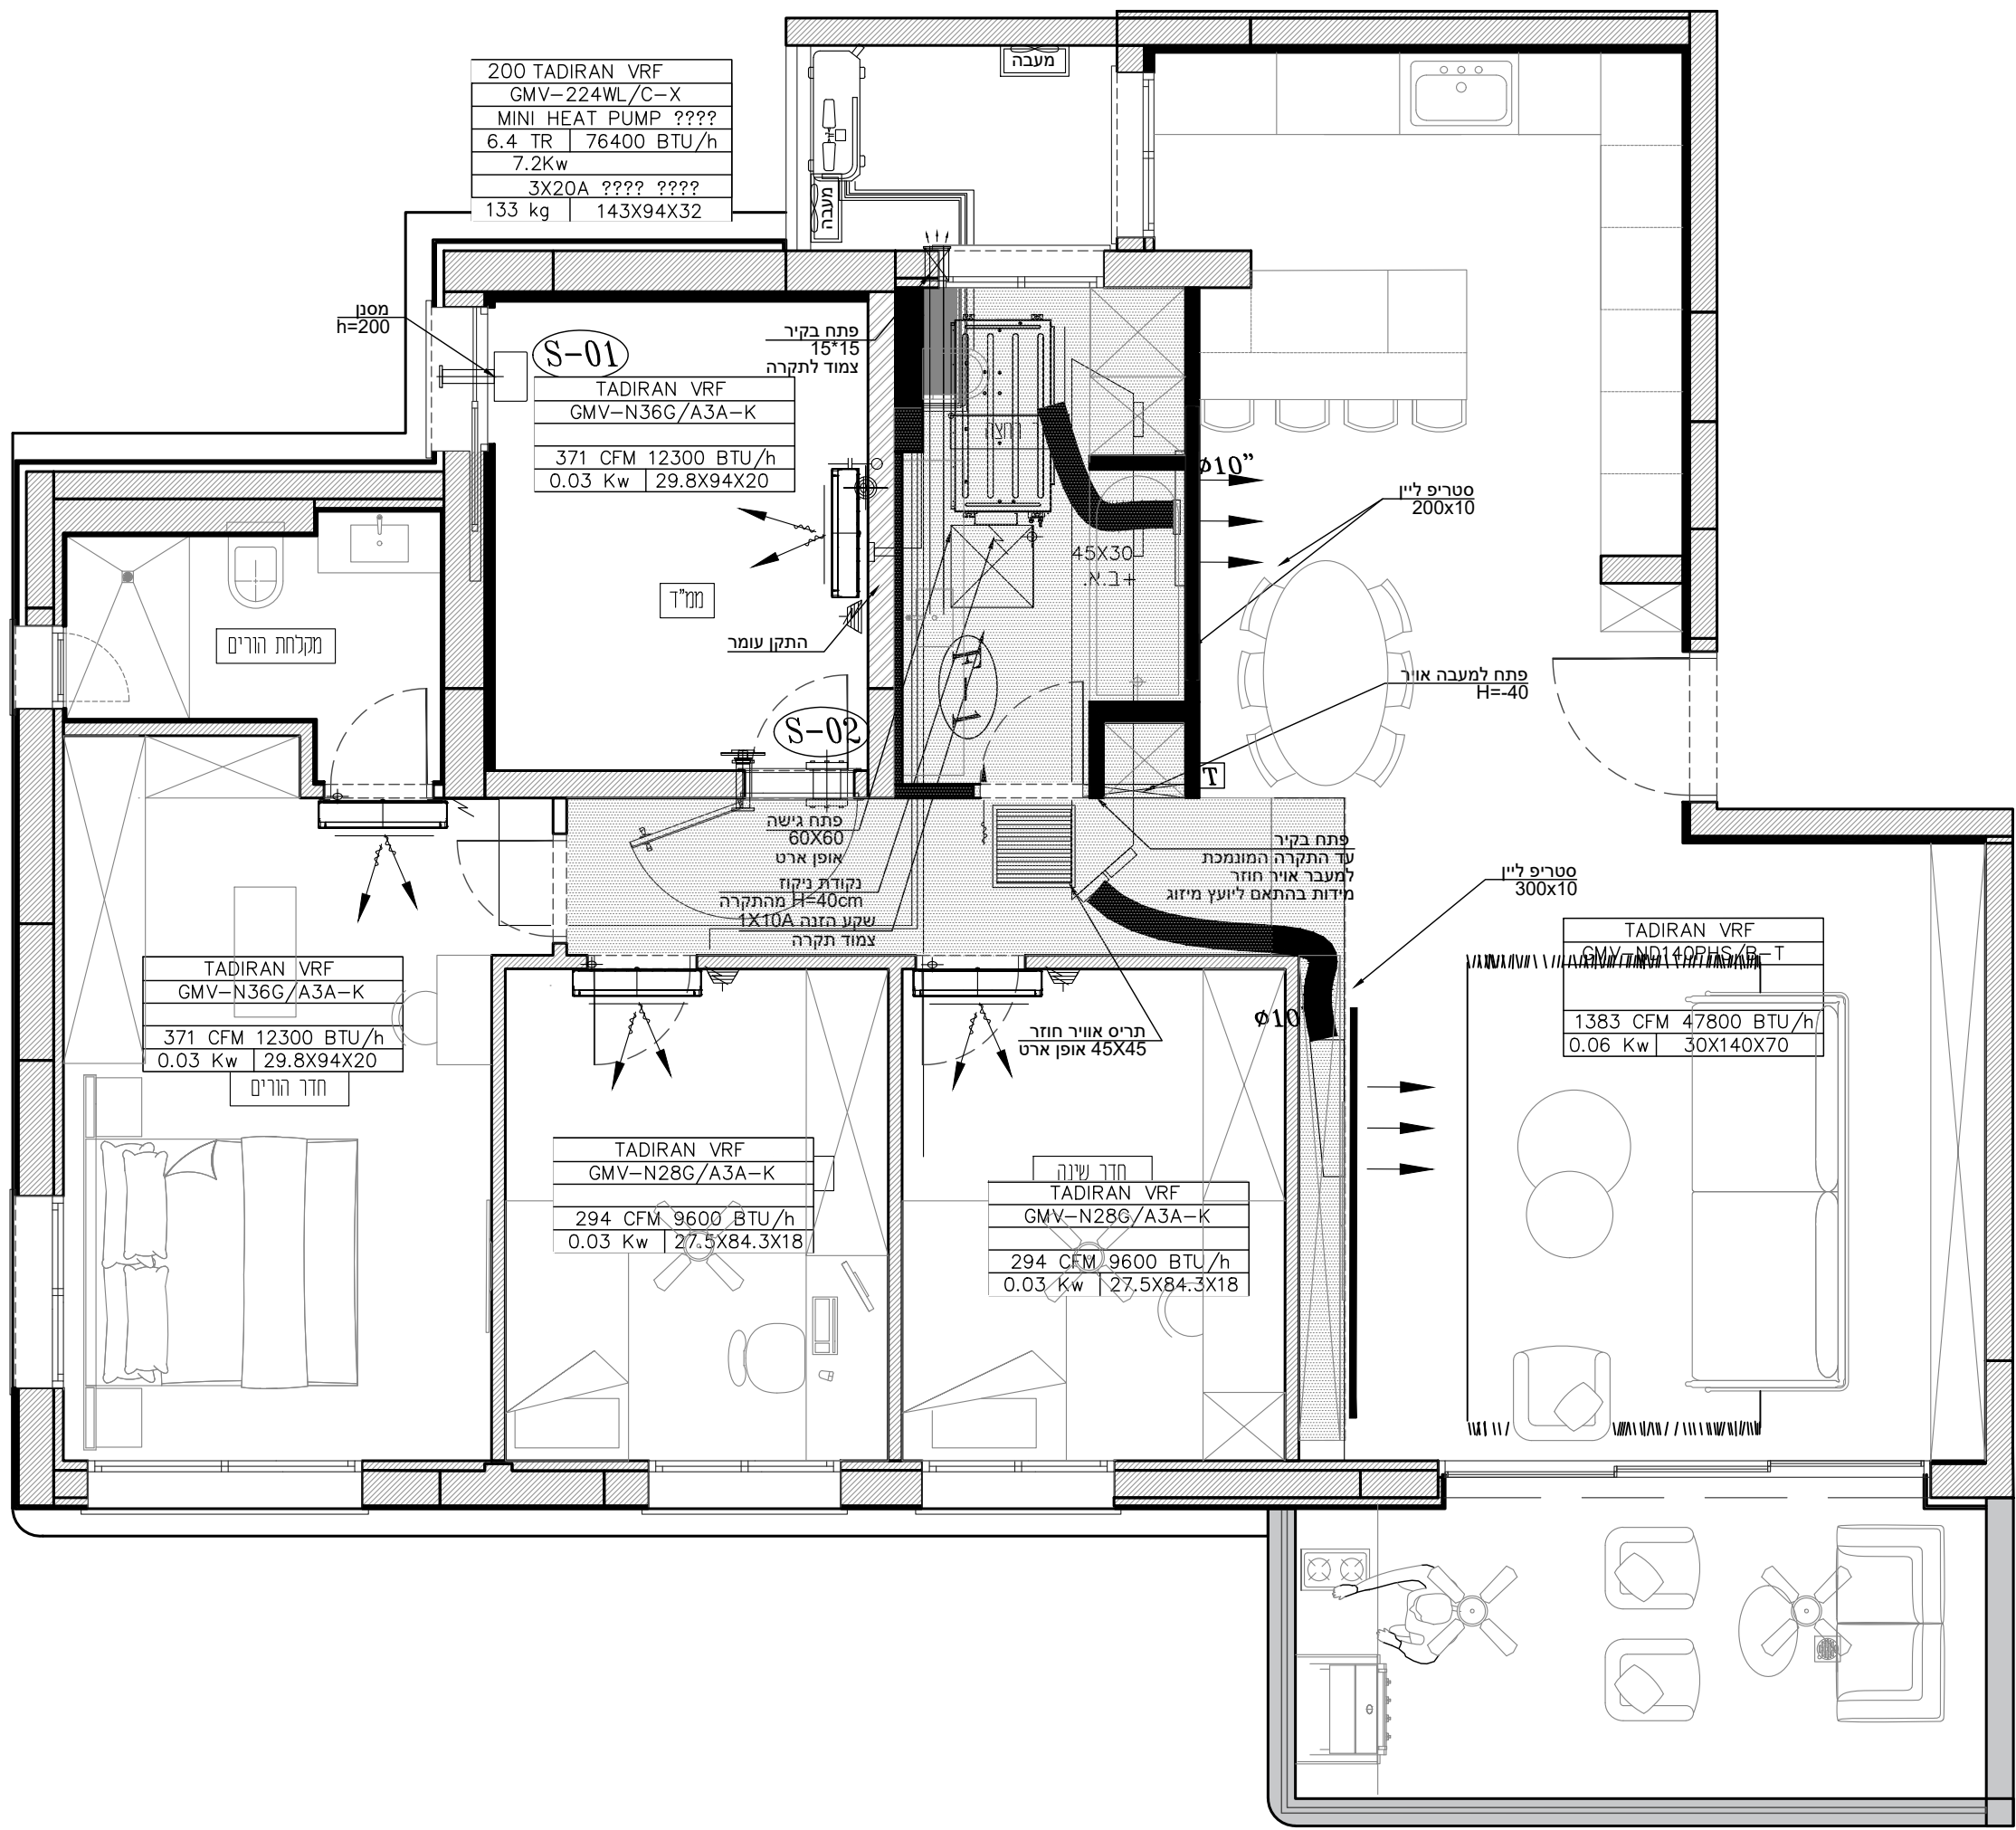

לקוח: ענבל ותומר		תכנית: מיזוג	
כתובת: הסבוראים 5 תל אביב		גיליון מס':	
05.08.2026	קנ"מ: 1:50	גודל גיליון: A2	
חתימת הלקוח לאישור התכנית:			
לעיון לאישור למכרז לביצוע			
1. על המבצע לבדוק את התאמת התכנית בשטח, לפני הבניה, ולבקר את המידות. על כל טעות ואזי אי התאמה יש לעדכן משרד מחכנו. 2. אין לקבוע מידות עפיי שרסוס. המידות המחייבות הן מידות שנמדדו בשטח לאחר ביצוע 3. המידות בתכנית הן ברוטו - ללא חיפוי גמר 4. יתכנו שנויים בהתאם להוראות הביצוע הסופי 5. כל התכניות נשארות רכוש המחכנו: אין לעשות בהן שימוש ללא אישור בכחב מהמחכנו 6. כל התערות חקפות אלא אם צויין אחרת			
מקרא מיזוג		מעקב שינויים	
הערות לתכנית מיזוג		מס'	תיאור השינוי
כל התערות חקפות אלא אם צויין אחרת • חיאום בשטח: על קבלן המיזוג לבצע חיאום מערכות מול קבלן הגבס, האינסטלציה והחשמל לפני חילולת ביצוע • אישור מיקומים: מיקום היחידות הפנימיות נמאיידים, פחחי השירות ומיקום הגרילים יסומנו באחר • יואשורו על ידי יועץ מזגנים בחיאום עם המעצב.ח לפני החקנה • מידות גרילים: המידות המצויינות בתכנית עבור הגרילים נדקוראסלוס) הן מידות "מחת אור" נטו. • יש לחאם מול איש המיזוג את גודל הפחת הנדרש בגבס בהתאם לסוג הגריל הנבחר • קו-אפס: גרילים המוחחקנים בחוך סיגרי גבס יוחקנו בקו ישר		1.	מס'
		2.	מס'
		3.	מס'
		4.	מס'
		5.	מס'
		6.	מס'
		7.	מס'
שטח חקרה מונמכת למיזוג		מס'	
מרכיבי ך מחלק אוויר		מס'	
מח מחיק בחקרת גבס		מס'	
ניקוח מים למזגן		מס'	
טרמוסטט שליטה		מס'	
גובה הנמכה מחקרה		מס'	
כיוון זרימת אוויר		מס'	



HMDAR GLIBSMAN SHROCHAT
INTERIOR DESIGN STUDIO
054-750654
hadar.glibsman@gmail.com